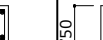
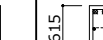


小梁リスト	特記無き限り、 1. 巾止筋は、D10@1000以内とする 2. スリーブ補強筋は、ダイヤレンNSを使用すること
-------	---

小梁リスト	特記無き限り、 1. 巾止筋は、D10@1000以内とする 2. スリーブ補強筋は、ダイヤレンNSを使用すること
-------	---

符号	B1	B1A		B2	B3	B4	B5	WCB1		WCB1A	WCB2		WCB2A		WCB2B		CG1	CG1A	CG2		CG2A	
位置	全断面	SX2端	中央・終端	全断面	全断面	全断面	全断面	元端	先端	全断面	元端	先端	元端	先端	元端	先端	全断面	全断面	元端	先端	元端	先端
断面																						
上端筋	4 - D22	4/2 - D22	4 - D22	3 - D22	3 - D22	5 - D22	3 - D22	2/2 - D16	2 - D16	2 - D16	2/2 - D19	2 - D19	2/2 - D22	2 - D22	2/2 - D22	2 - D22	4 - D35	5 - D25	5/3 - D25	5 - D25	5/3 - D25	5 - D25
下端筋	4 - D22	4 - D22	4 - D22	3 - D22	3 - D22	5 - D22	3 - D22	2 - D16	2 - D16	2 - D16	2 - D19	2 - D19	2 - D22	2 - D22	2 - D22	2 - D22	4 - D35	5 - D25	5 - D25	5 - D25	5 - D25	5 - D25
STP	2 - D10 @150	2 - D10 @150		2 - D10 @200	2 - D10 @200	2 - D13 @200	2 - D10 @200	2 - D10 @200		2 - D10 @200	2 - D10 @200		2 - D10 @200		2 - D10 @200		2 - D13 @200	2 - D13 @200	2 - D13 @200		2 - D13 @200	
腹筋	2 - D10	2 - D10		2 - D10	2 - D10	2 - D10	2 - D10	2 - D10		2 - D10	2 - D10		2 - D10		2 - D10		2 - D10	2 - D10	2 - D10		2 - D10	

符号	CG3		CG3A		CG4		CG5		CG6	CG7	
位置	元端	先端	元端	先端	元端	先端	元端	先端	全断面	元端	先端
断面											
上端筋	7/3 - D25	7 - D25	7/3 - D25	7 - D25	2/2 - D19	2 - D19	7/4 - D25	7 - D25	3 - D29	3/2 - D25	3 - D25
下端筋	7 - D25	7 - D25	7 - D25	7 - D25	2 - D19	2 - D19	7 - D25	7 - D25	3 - D29	3 - D25	3 - D25
STP	2 - D13 @150		2 - D13 @150		2 - D10 @200		2 - D13 @150		2 - D13 @200		
腹筋	2 - D10		2 - D10		2 - D10		2 - D10		2 - D10		

スラブリスト


符号	スラブ厚 (mm)	位置	主筋方向	配力筋方向	備 考 (L : 許容出寸法)
S1	180	上端筋	D10D13@200	D10@200	
		下端筋	D10@200	D10@200	
S2	180	上端筋	D13@200	D10D13@200	
		下端筋	D10D13@200	D10@200	
S3	200	上端筋	D13@200	D10@200	
		下端筋	D10@200	D10@200	
S4	250	上端筋	D16@100	D13@150	
		下端筋	D16@100	D13@150	
S5	250	上端筋	D13@100	D13@100	
		下端筋	D13@100	D13@100	
S6	250	上端筋	D13@150	D13@150	
		下端筋	D13@150	D13@150	
S7	250	上端筋	D13@100	D13@150	
		下端筋	D13@100	D13@150	
		上端筋			
		下端筋			
CS1	210～180	上端筋	D13@200	D10@200	先端溝下スラブ厚130mm以上とする L=1600mm
		下端筋	D10@200	D10@200	
CS1A	210～180	上端筋	D13@100	D10@200	先端溝下スラブ厚130mm以上とする L=1350mm
		下端筋	D10@100	D10@200	
CS2	210～180	上端筋	D13@100	D10@200	先端溝下スラブ厚130mm以上とする L=1950mm
		下端筋	D10@100	D10@200	
CS3	210～180	上端筋	D13@100	D10@200	先端溝下スラブ厚130mm以上とする L=1100mm
		下端筋	D10@100	D10@200	
CS4	250～250	上端筋	D13@100	D13@200	L=1200mm
		下端筋	D13@100	D13@200	
CS5	150～150	上端筋	D10@200	D10@200	シングル配筋とする L=600mm
		下端筋	D10@200	D10@200	
CS6	250～250	上端筋	D16@150	D13@150	L=2000mm
		下端筋	D13@150	D13@150	
CS7	200～200	上端筋	D13@150	D10@200	L=1200mm
		下端筋	D10@150	D10@200	
CS8	250～250	上端筋	D13@100	D13@150	L=1200mm
		下端筋	D13@100	D13@150	
		上端筋			
		下端筋			
		上端筋			
		下端筋			
		上端筋			
		下端筋			

壁リスト

壁リスト 特記なき限り、 1. 巾止筋はD10@1000以内とする

[illegible]

開口補強筋要領

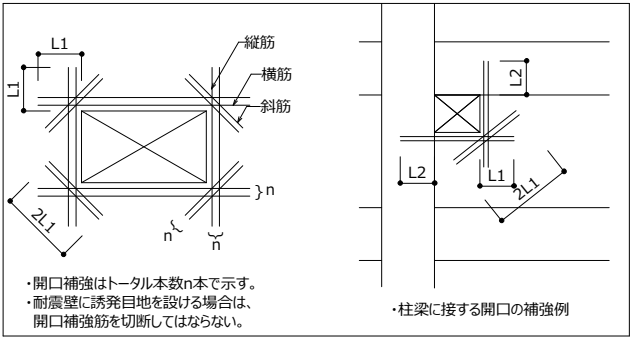


壁端部補強筋

壁端部補強筋 特記なき限り、1.階段壁（KW25）の端部補強筋は基礎梁底まで定着させる 基礎梁天端増打内耐震壁配筋要領

全階共通		
W16,W17,W18	2-D13	4-D13
W20	2-D16	4-D16
KW25	4-D16	-
断面		

基礎梁天端増打内耐震壁配筋要領

※壁リスト中のKW25及びW30A,W30Bの横筋は
構造躯体天端から配筋すること
(打増し内にも横筋を配筋する)

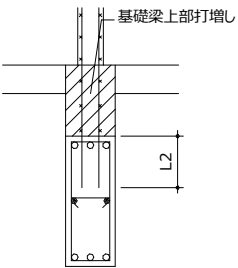

確認	設計図書の法適合確認	改訂日付	説明	改訂日付	説明	備考	矢作建設工業株式会社一級建築士事務所 愛知県知事登録 (U-3) 第1618号 一級建築士大臣登録 第256203号 平山 政雄 承認1 承認2 承認3 担当 製図 平山 野田 梶原 菅沼田 藤井	工事名称 (仮称) 愛知県名古屋市長和区山手通四丁目計画	設計No. 221098	図面No. S-1406
	【構造関係規定に適合することを確認】	26.01.19	実施設計図書					図面名称 【S棟】小梁・片持梁・床・壁リスト 縮尺 A3=1/100	発行日 26.04.21	
	構造設計一級建築士 交付 第2007号 梶原 卓行	26.04.21	第1回修正図書							